


AP-01-01. Банный блок у газобетонного торца · концепция v01

Парная → помывочная → зимняя зона отдыха. Геометрия учитывает холодный зазор и слои теплой капсулы до чистовых размеров.


СТАТУС: КОНЦЕПЦИЯ

Не для закупки, разметки и монтажа

1. План банного торца, М 1:35

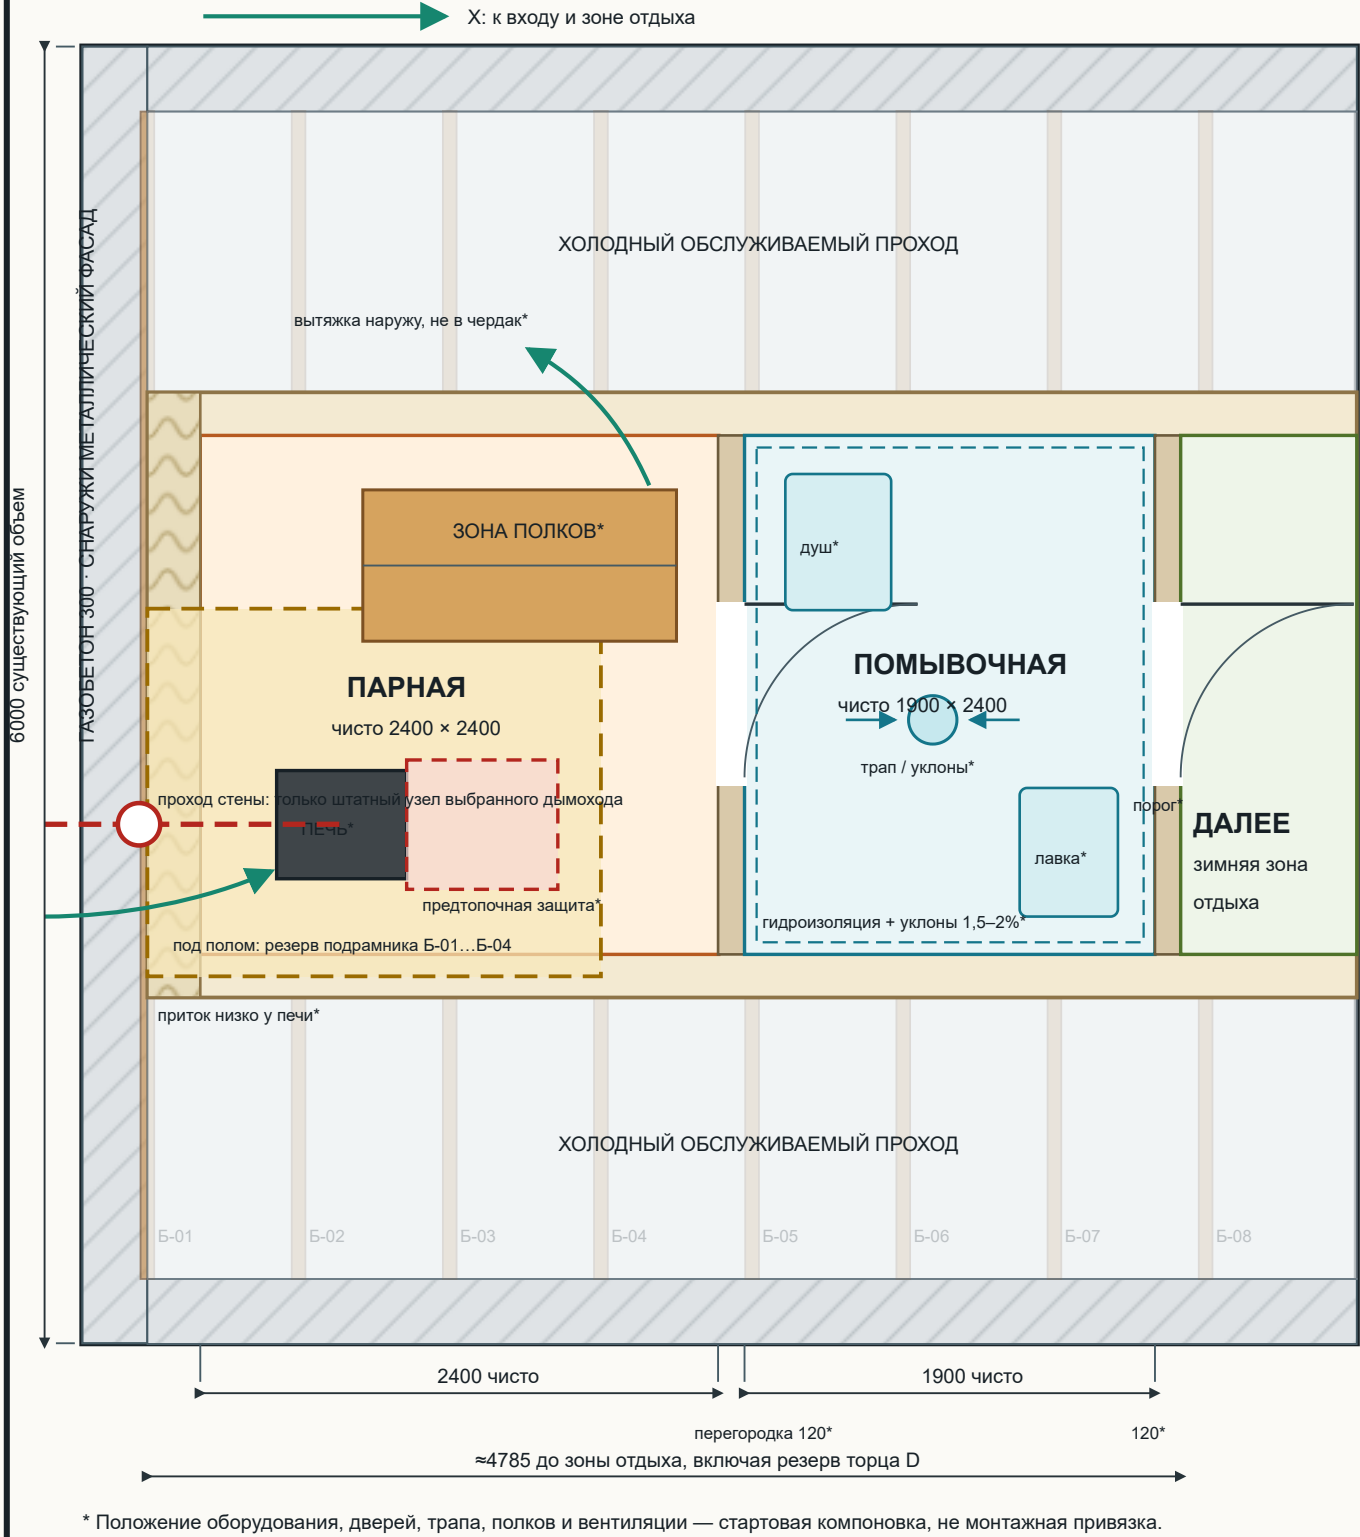

2. Поперечный разрез парной/помывочной, М 1:50

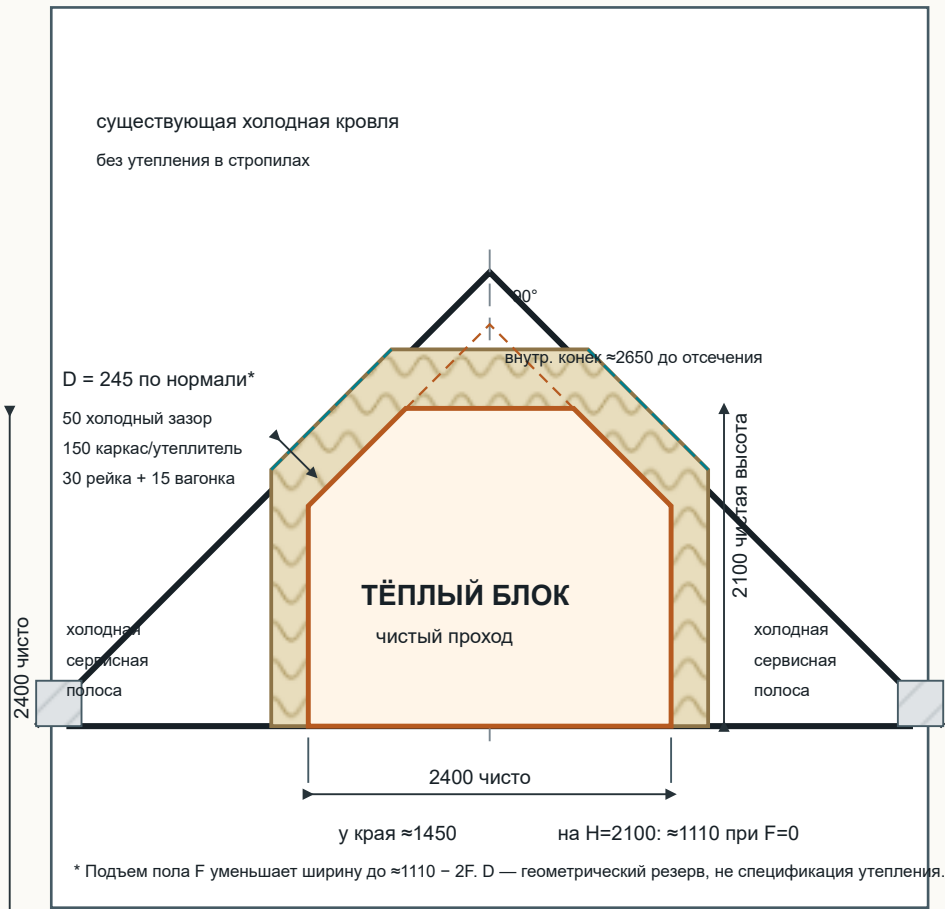

Принято на v01

- парная у X=0, затем помывочная;
- чистая ширина обоих помещений 2400;
- парная 2400, помывочная 1900;
- центральный плоский потолок 2100;
- по бокам остаются холодные проходы.

Параметры до следующей ревизии

- Р — модель, масса, габарит и отступы печи.
- СН — диаметр и единая система дымохода.
- G — пирог газобетонного торца и фасада.
- T — утепление после теплового расчета.
- F — отметка и несущая схема нового пола.
- V/D — вентиляция и фактическая точка слива.

До рабочего узла нельзя

- резать/дублировать балки и связи кровли;
- покупать печь, дымоход и утеплитель;
- вести одностенную трубу через стену;
- выпускать влажный воздух в чердак;
- считать перемычки расчетом перекрытия.

Отложенный контроль

Перед листом входа напомнить и обмерить проем/ригели между Б-16 и Б-18.

Сейчас банный торец это не блокирует.

Основание решения

МЧС: печь, лист 500×700 минимум, разделки.

Kingspan: фольга/герметизация/зазор.

Подробнее: planning/bath_block_concept_v01.md

3. Зона печи: опора ≠ пожарная защита

