


А-3D-102. Общая схема: чердак 12 х 6 м, зоны бани, слои и наружный сэндвич-дымоход

Цель: увидеть все вместе в пропорциях. Это обзорный лист; узлы и размеры будут отдельными проверяемыми листами.

Пропорции учтены: чердак 12 000 х 6 000, высота 3 000

Зоны по длине: 2400 парная + 2000 помывочная + 7600 отдых/вход

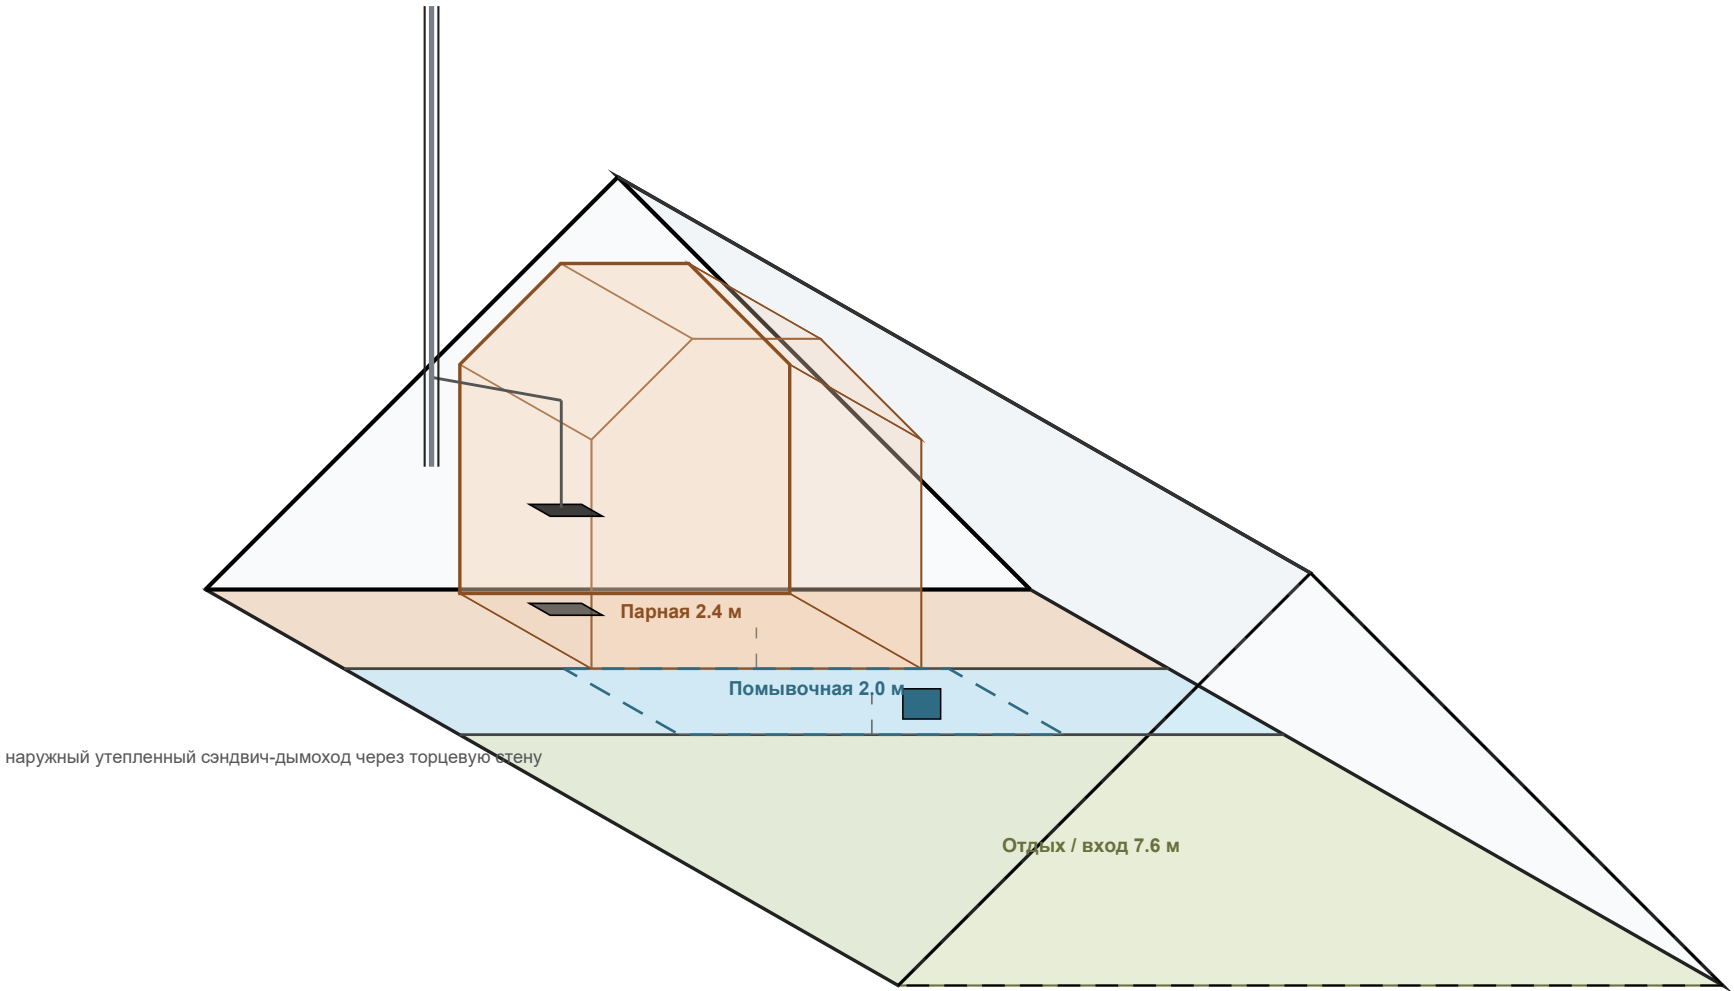

Пирог ската: снаружи внутрь

- металл / кровля
- вентзасор V 50-100
- утепление Т 150-200+
- фольга, швы проклеить
- контррейка 20-30
- вагонка 14-16

Что уже заложено в общий лист

- Чистая парная: 2400 х 2400.
- Край парной по высоте: ~1666.
- Зона 2100+ внутри: ~1531.
- Потеря внутрь по нормали: 95.
- Бойлер не на чердаке.
- Помывочная легкая, слив 50 вниз.
- Пар не выпускать в подкровелье.
- Печь/дымоход/пол - отдельные узлы.